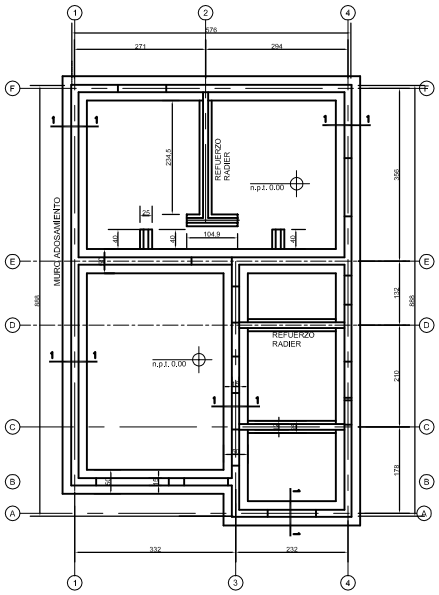

PLANTA FUNDACIONES
Escala1:50

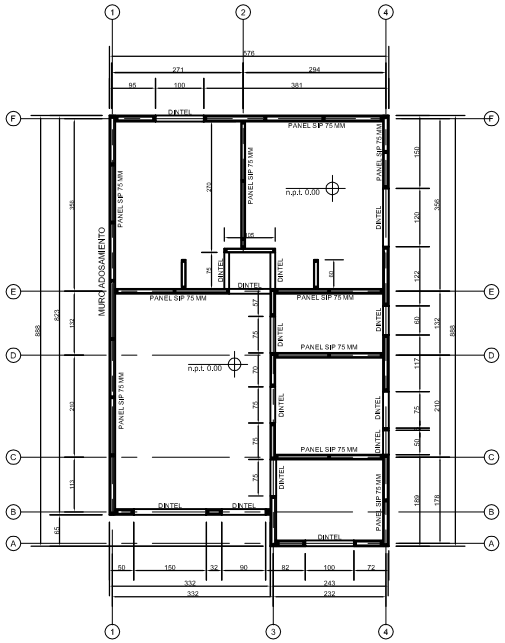

PLANTA ESTRUCTURA
Escala1:50

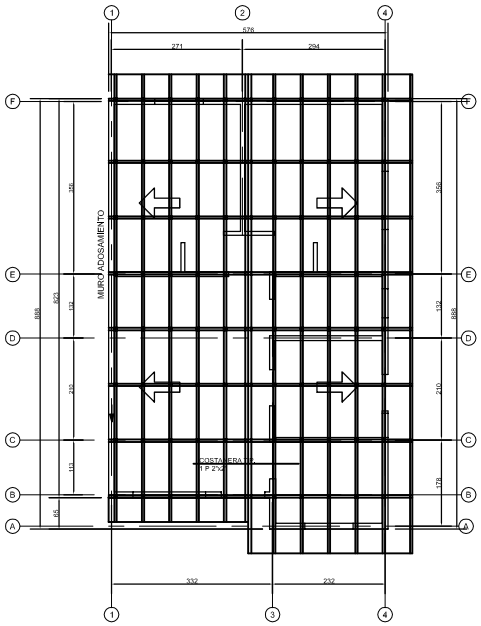

PLANTA TECHUMBRE
Escala1:50

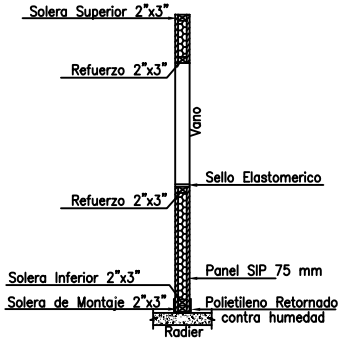

DETALLE SIP VANO
Escala1:20

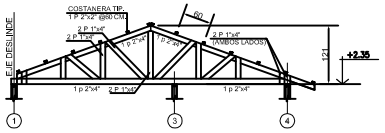

ELEVACION CERCHA
Escala1:50

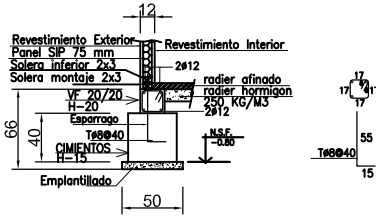

DETALLE SECCION 1
Escala1:20

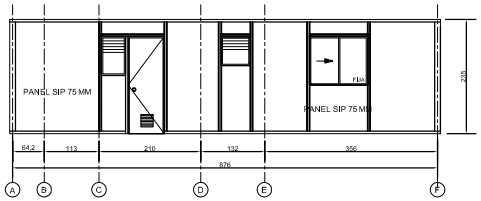

ELEVACION EJE 4
Escala1:50

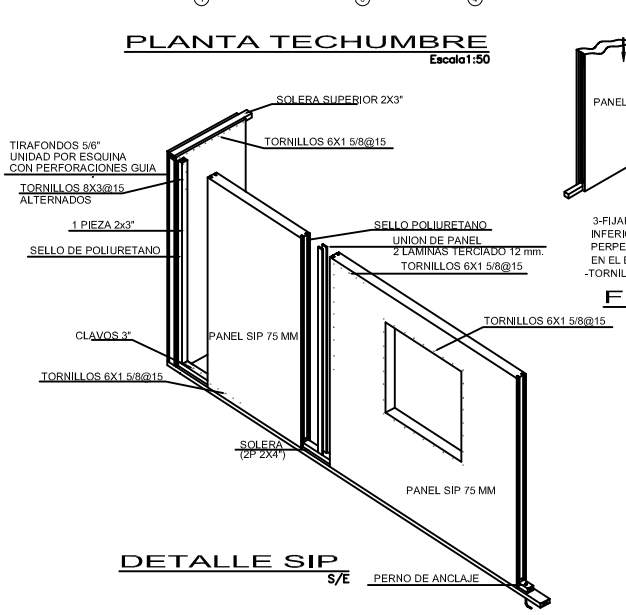

DETALLE SIP
S/E

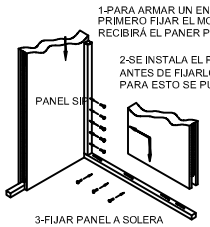

1-PARA ARMAR UN ENCUENTRO ESQUINA, PRIMERO FIJAR EL MONTANTE QUE RECIBIRÁ EL PANER PERPENDICULAR.

2-SE INSTALA EL PANER PERPENDICULAR, ANTES DE FIJARLO SE DEBE RECTIFICAR EL PLANO. PARA ESTO SE PUEDE UTILIZAR UN LISTON AUXILIAR.

3-FIJAR PANEL A SOLERA INFERIOR Y AL PANEL PERPENDICULAR EN EL ENCUENTRO CON EL MONTANTE,
-TORNILLO #6X11/4"@15cm.

FIJACION PANEL SIP
S/E

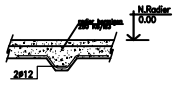

REFUERZO RADIER
Escala1:20

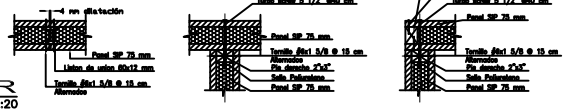

DETALLES ENCUENTROS TIPICOS
Escala1:1

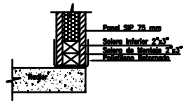

DETALLE CONTRA HUMEDAD
Escala1:1

N°	NOTAS.-
1.-	DIBUJO.-
	1.1.- Cotas en cms.-
	1.2.- Dimensión de fierros en mms.-
	1.3.- Niveles en mts.-
	1.4.- Cotas prevalecen sobre escalímetro.-
	1.5.- Verificar Medidas de los Cerchos en Terreno.-
2.-	HORMIGONES
	2.1.-Emplantillado Hormigón Calidad H-5.-
	2.2.-Cimiento.-Sobrecimiento Hormigón Calidad H-25 con f'c=20 (Mpa) 90% de nivel .-
	2.3.-Radier Calidad H° 15.-
	2.4.-Recubrimiento mínimo 2.5 cm. en pilares y vigas, 3.0 cm. en fundaciones.-
3.-	ACERO
	3.1.-Acero de Refuerzo A 63-42 con Resaltes para Hormigones .-
	3.2.-Acero estructural A42-27ES, perfiles plegados .-
4.-	TECHUMBRE
	4.1.-Verificar Cotas en Terreno antes de la Fabricación de Cerchos.-
	4.2.-Para Tijerales y Cerchos se Recomienda Piezas de Pino Según Planta Techumbre.-
5.-	MADERA
	5.1.-Tabiquería de madera en plano.-
	5.2.-Madera pino radiata grado estructural G1 humedad 12% max.-

VVL PROYECTOS DE INGENIERIA CIVIL

N°	OBSERVACIONES	DIB.	REV	CAL.

DIBUJO:	I. BUSTOS H. DIBUJANTE PROYECTISTA	PROYECTO: PROYECTO POBLACIÓN EL NUEVO ESFUERZO SECTOR BERTA III - CORONEL
REVISO:	VICTOR VILLAGRAN L. INGENIERO CIVIL	PROPIETARIO: CONSTRUCTORA EL NUEVO ESFUERZO VIVIENDA TIPO A
CALCULO:	VICTOR VILLAGRAN L. INGENIERO CIVIL	CONTENIDO: PLANTAS DE FUNDACIONES, ESTRUCTURA Y TECHUMBRE ENVIGADO PISO, ELEVACIONES,SECCIONES Y DETALLES
		FECHA: MARZO 2015 · ESCALA: INDICADAS · REV: B · LAM. 1 DE 1