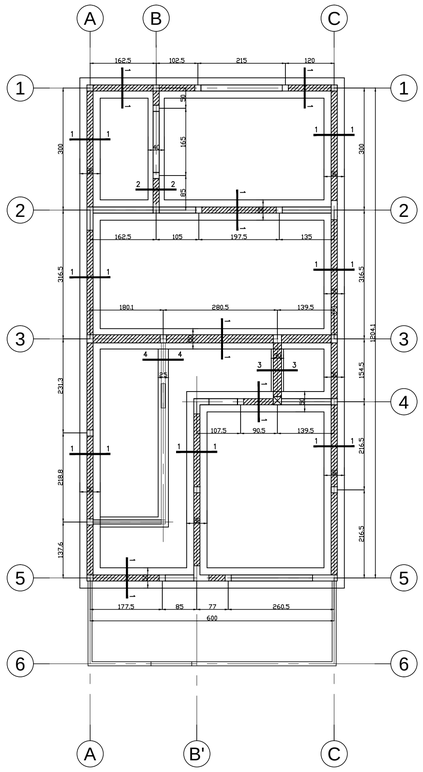

PLANTA FUNDACIONES
Escala1:50

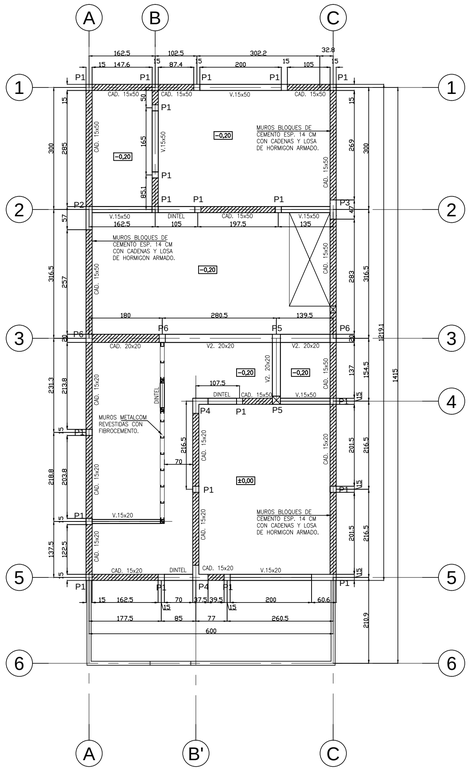

PLANTA ESTRUCTURA 1° PISO
Escala1:50

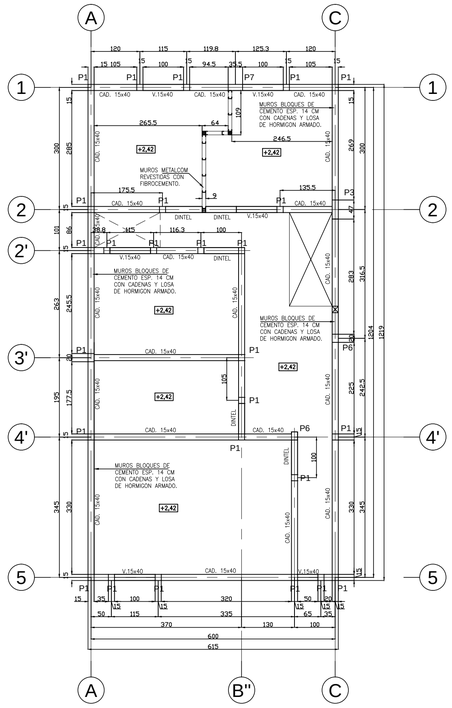

PLANTA ESTRUCTURA 2° PISO
Escala1:50

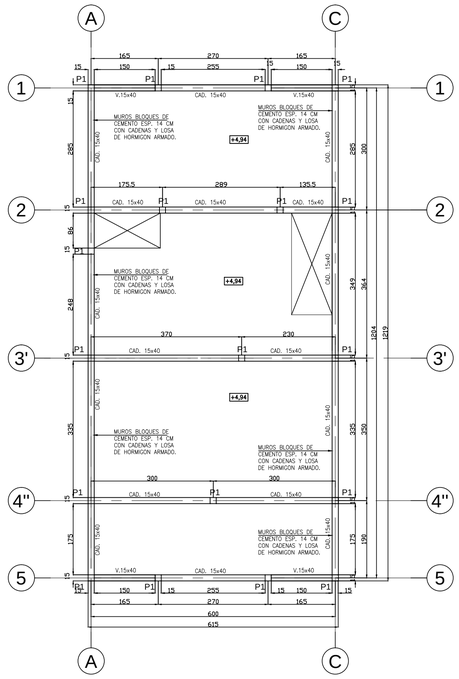

PLANTA ESTRUCTURA 3° PISO
Escala1:50

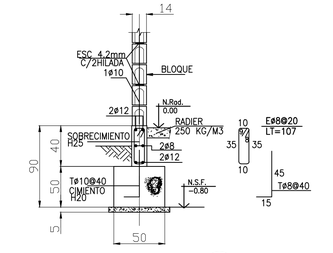

SECCION 1
ESC. 1:20

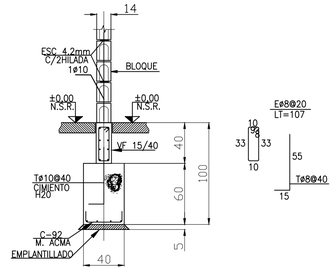

SECCION 2
ESC. 1:20

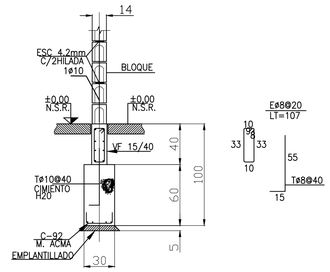

SECCION 3
ESC. 1:20

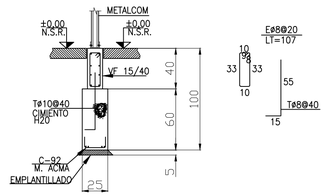

SECCION 4
ESC. 1:20

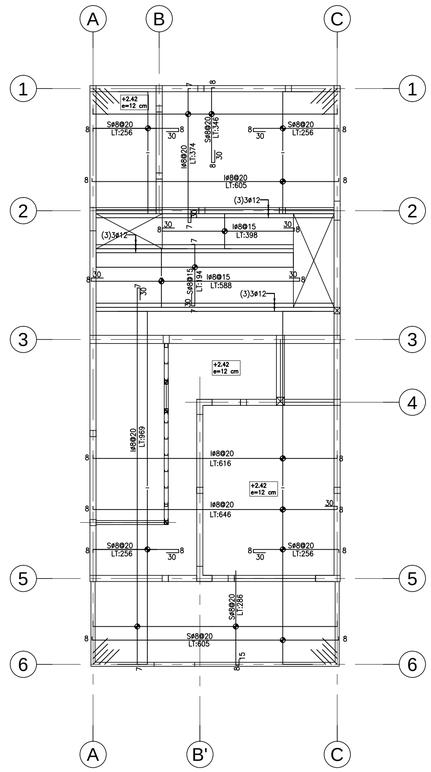

PLANTA ESTRUCTURA LOSA 1
Escala1:50

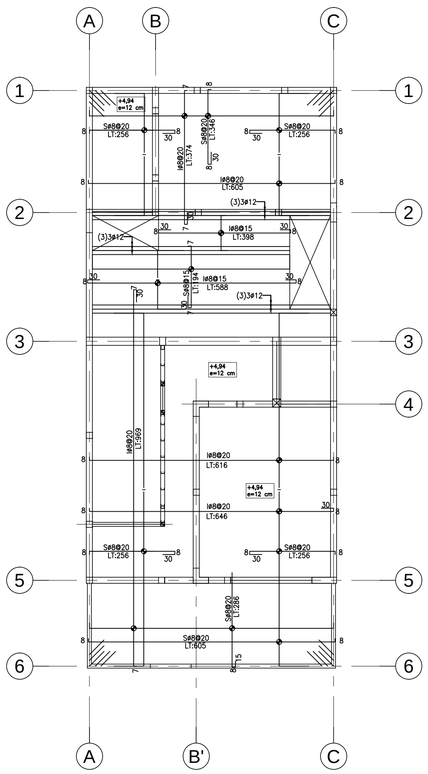

PLANTA ESTRUCTURA LOSA 2
Escala1:50

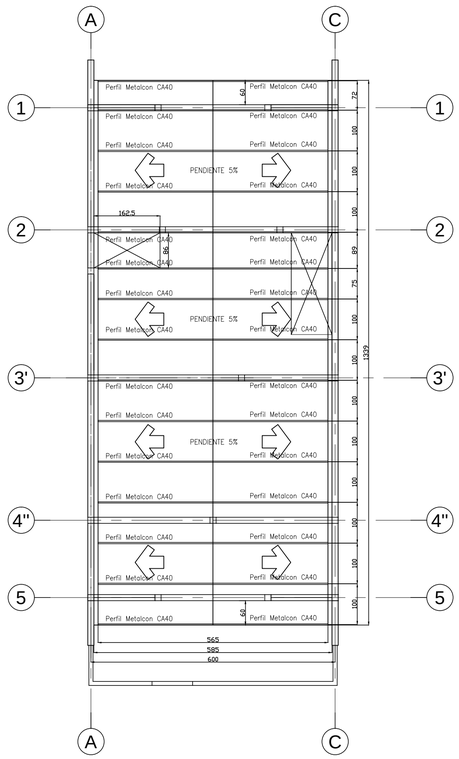

PLANTA TECHUMBRE
Escala1:50

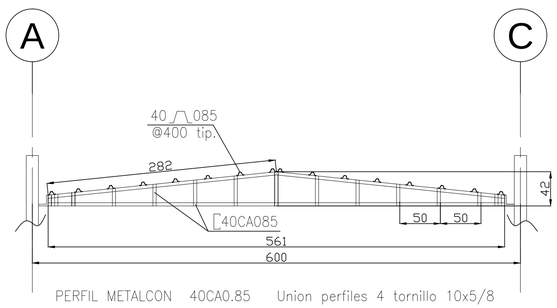

CERCHA
Escala1:25

CONTENIDO	CERTIFICADO DE INFORMACIONES PREVIAS	PROYECTO:	ESTRUCTURA REGULARIZACIÓN PIZZERIA EL PADRINO
	NUMERO: 1398/20016 — FECHA: 07/05/2017	FECHA: Enero 2017	ESCALAS: INDICADAS
	INFORMACIÓN PROPIEDAD		INGENIERO CIVIL: ARTURO MENDEZ VELOZO RUT: XXXXXX
	CALLE: LA FLORIDA — NUMERO: 11 — ROL AVALUO: 5340-1		REPRESENTANTE LEGAL: CRISTOFER GOMEZ SANTANDER RUT: 15.578.280-3
	SITIO: — MANZANA: A — LOTE: 1	APARICIO, ARQUITECTURA, INGENIERÍA Y CONSTRUCCIÓN RUT: 76.533.368-7	NORTE
	COMUNA: Antofagasta — PROVINCIA: Antofagasta — CIUDAD: Antofagasta		LAMINA Nº X
	CORREO : aparicio.proyectos@gmail.com		DE:XXXX