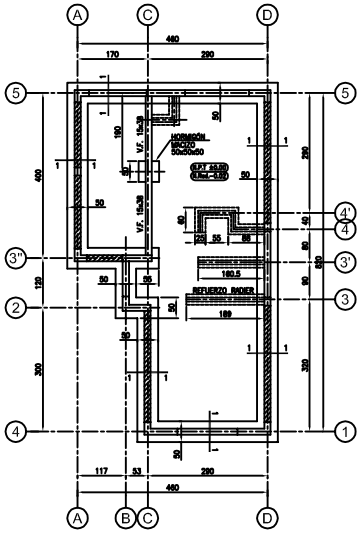

PLANTA FUNDACIONES
Escala1:50

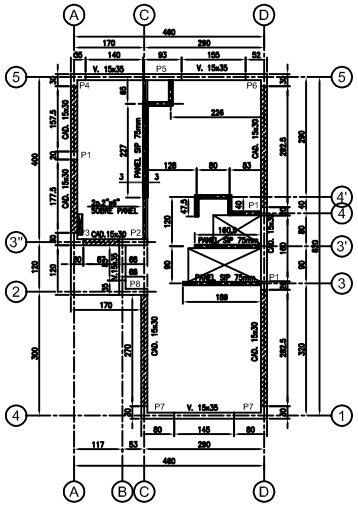

PLANTA ESTRUCTURA NIVEL 1
Escala1:50

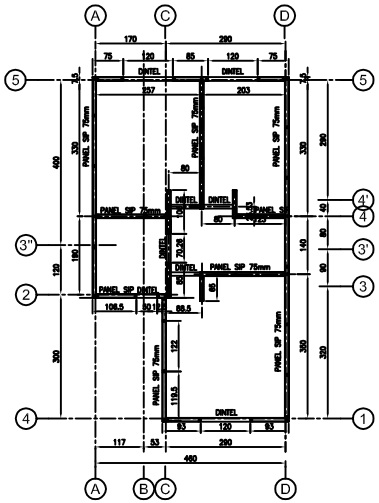

PLANTA ESTRUCTURA NIVEL 2
Escala1:50

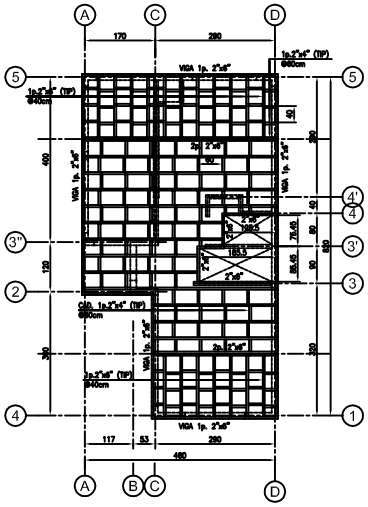

PLANTA ENVIGADO PISO
Escala1:50

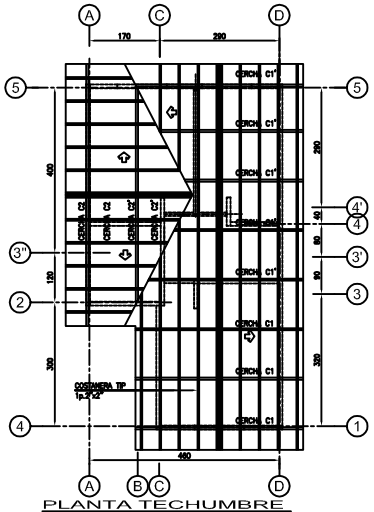

PLANTA TECHUMBRE
Escala1:50

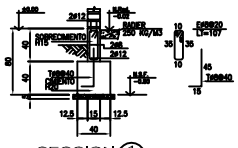

SECCION 1
ESC. 1:25

V.F. 15x38
Esc 1:25

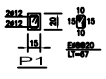

P1

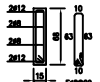

P2

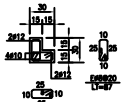

P3

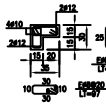

P4

P5

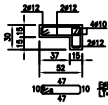

P6

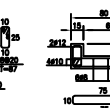

P7

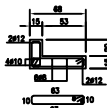

P8

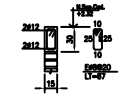

CAD.15x30
Escala1:25

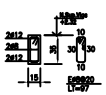

V.15x35
Escala1:25

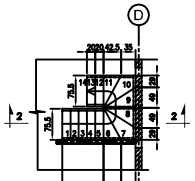

PLANTA ESCALERA
Escala1:50

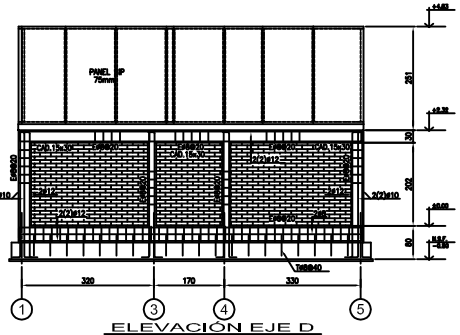

ELEVACIÓN EJE D
Escala1:50

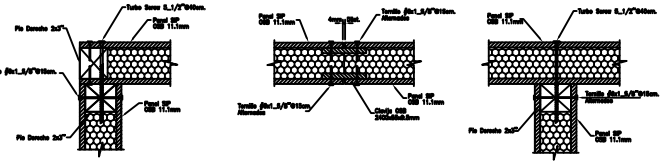

DETALLES ENCUENTROS TIPICOS
S/E

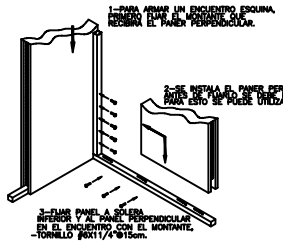

PROCESO FIJACION PANEL SIP
S/E

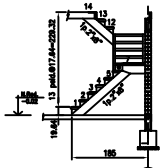

SECCION 2
ESC. 1:25

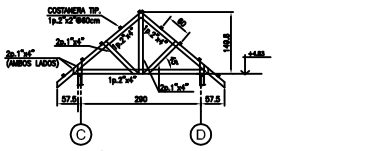

ELEVACIÓN CERCHA C1
Escala1:50

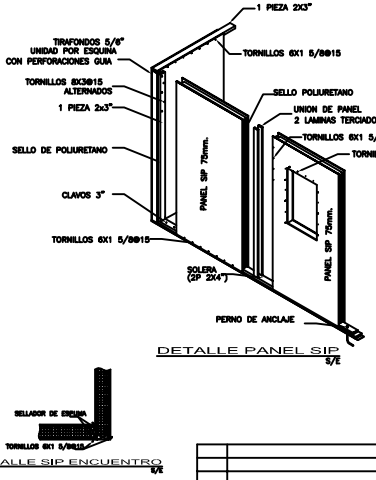

DETALLE PANEL SIP
S/E

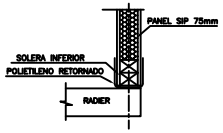

PROTECCION CONTRA HUMEDAD
S/E

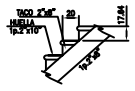

DETALLE PELDAÑO
Escala1:25

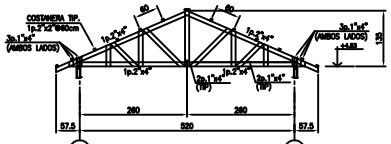

ELEVACIÓN CERCHA C2
Escala1:50

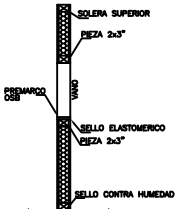

DETALLE SIP VANO
S/E

DETALLE SIP ENCUENTRO
S/E

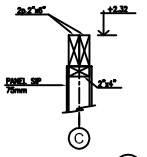

SECCION 3
ESC. 1:10

COMENTARIOS
MARZO 2015

N°	NOTAS:-
1.-	DIBUJO.--
	1.1.-- Cotas en cms.--
	1.2.-- Dimensión de Barras en mms.--
	1.3.-- Niveles en mts.--
	1.4.-- Cotas prevalecen sobre coordinadas.--
	1.5.-- Verificar Medidas de los Cercha en Terreno.--
2.--	HORMIGONES
	2.1.--Especificación Hormigón Calidad H-5.--
	2.2.--Cimiento.--Especificación Hormigón Calidad H-25 con Tm=30 (Bajo) NCh 170 de nivel .--
	2.3.--Radier Calidad H° 15.--
	2.4.--Recubrimiento mínimo 2,5 cm. en pilares y vigas, 3,0 cm. en fundaciones.--
3.--	ACERO
	3.1.--Acero de Refuerzo A 63-42 con Resales para Hormigones .--
	3.2.--Acero estructural A42-27ES, perfiles abiertos .--
4.--	TECHUMBRE
	4.1.--Verificar Cotas en Terreno antes de la Fabricación de Cerchas.--
	4.2.--Para Tijerales y Cerchas en Recomienda Placas de Fibra Rugda Plasta Techumbre.--
5.--	MADERA
	5.1.--Tratamiento de madera en obra.--
	5.2.--Madera pino radata grado estructural 01 humedad 12% max.--

VVL PROYECTOS DE INGENIERIA CIVIL

N°	OBSERVACIONES	DIB.	REV	CAL

DIBUJO:	L BUSTOS H DIBUJANTE PROYECTISTA
REVISO:	VICTOR VILLAGRAN L INGENIERO CIVIL
CALCULO:	VICTOR VILLAGRAN L INGENIERO CIVIL

PROYECTO: PROYECTO POBLACIÓN EL NUEVO ESFUERZO SECTOR BERTA III - CORONEL

PROPIETARIO: CONSTRUCTORA EL NUEVO ESFUERZO VIVIENDA TIPO A

CONTENIDO : PLANTAS DE FUNDACIONES, ESTRUCTURA Y TECHUMBRE ENVIGADO PISO, ELEVACIONES,SECCIONES Y DETALLES

FECHA : MARZO 2015 | ESCALA : INDICADAS | REV : B | LAM. 1 DE 1