LOCAL AUTOMOTRIZ

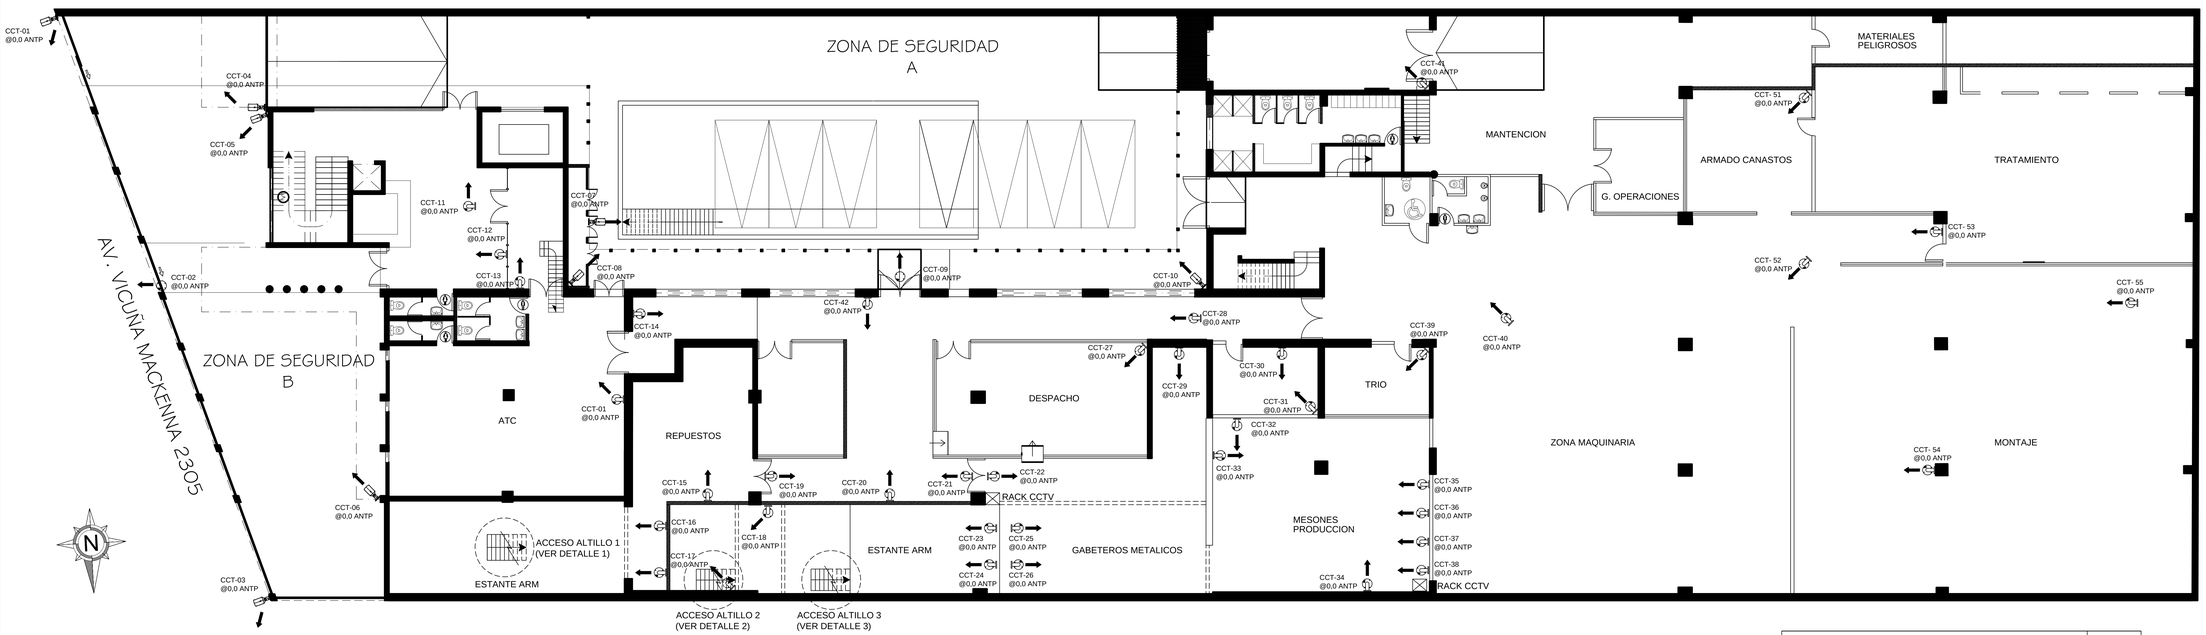

PLANTA PRIMER PISO

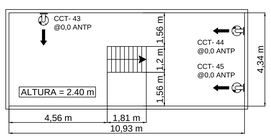

DELALLE 1
PLANTA ALTILLO 1

DELALLE 2
PLANTA ALTILLO 2

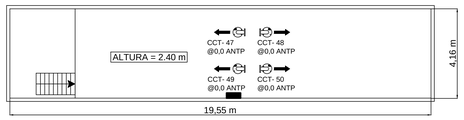

DELALLE 3
PLANTA ALTILLO 3

SIMBOLOGIA	CANT.
CAMARA TIPO BALA IP DE EXTERIOR CON ZOOM PARA MONTAR EN LA PARED USA CABLE CAT Y TOMA DE CORRIENTE.	8
CAMARA TIPO PTZ IP DE INTERIOR CON ZOOM PARA MONTAR EN LA PARED USA CABLE CAT Y TOMA DE CORRIENTE.	2
CAMARA TIPO DOMO IP DE INTERIOR CON ZOOM PARA MONTAR EN LA PARED USA CABLE CAT Y TOMA DE CORRIENTE.	45
GABINETE RACK MURAL PARA INSTALACION OPTIMIZA ESPACIOS Y RAPIDO ACCESO A LOS EQUIPOS.	2

LHRIASIM
SERVICIOS Y ASESORIAS DE REDES
SEGURIDAD - MONTAJES

PROYECTO
INSTALACION DE CAMARAS MEGALUX

PROPIETARIO :
MEGALUX

UBICACION :
AV. VICUÑA MACKENNA Nº 2305

COMUNA :
SAN JOAQUIN

ROL DE AVALUO
201-005

MOD. Nº	FECHA	OBSERVACIONES
VoBo		
VoBo		
APROBO	M.C.M.	
REVISO	M.C.M.	
DIBUJO	I.B.H	
PROYECTO		
	POR	FECHA	FIRMA

CONTENIDO
PLANTA PRIMER NIVEL DISTRIBUCION DE CAMARAS

MANDANTE :
NOMBRE: MEGALUX S.A.
R.LEGAL: SEBASTIAN SCHROTER M.
16.095.870-7
DOMICILIO: AV. SALVADOR Nº 726
COMUNA: PROVIDENCIA

ARQUITECTO
MARCELO COSMELLI M.
DIRECCION :
MINISTRO CARVAJAL N 27
PROVIDENCIA STGO.
FONO : 8137762

FECHA DICIEMBRE/2025
ESCALAS 1/50

ACAD.2012- MEGALUX-CAMARAS.DWG

Nº LAMINA
1 DE 3